



D4

ADA Paths of Travel

This diagram outlines the egress strategy for the first floor, emphasizing continuous path-of-travel, turning radii, and accessible slope conditions in accordance with ADA and ICCA117.1 standards. The primary egress path is distributed along the perimeter and through the central circulation spine, providing clear and direct routes from all occupied spaces to exits at the street edge.

Egress circulation is designed to maintain minimum clear widths throughout, ensuring unobstructed movement during evacuation while accommodating high occupant flow. Ramps integrated into the topographic floor condition follow code-compliant slopes, maintaining a maximum 1:12 gradient with level landings at required intervals. These transitions allow the building to negotiate elevation changes without interrupting accessibility or egress continuity.

Turning radii are embedded at key nodes along the path, particularly at corridor intersections, elevator lobbies, and points of directional change, allowing for full maneuverability and compliance with wheelchair accessibility standards. Rather than isolating these requirements, the system is integrated into the overall spatial logic, aligning circulation, topography, and code into a cohesive ground-level egress framework.

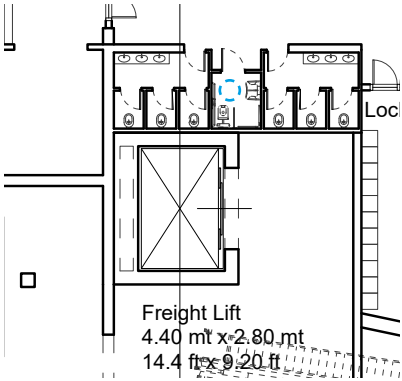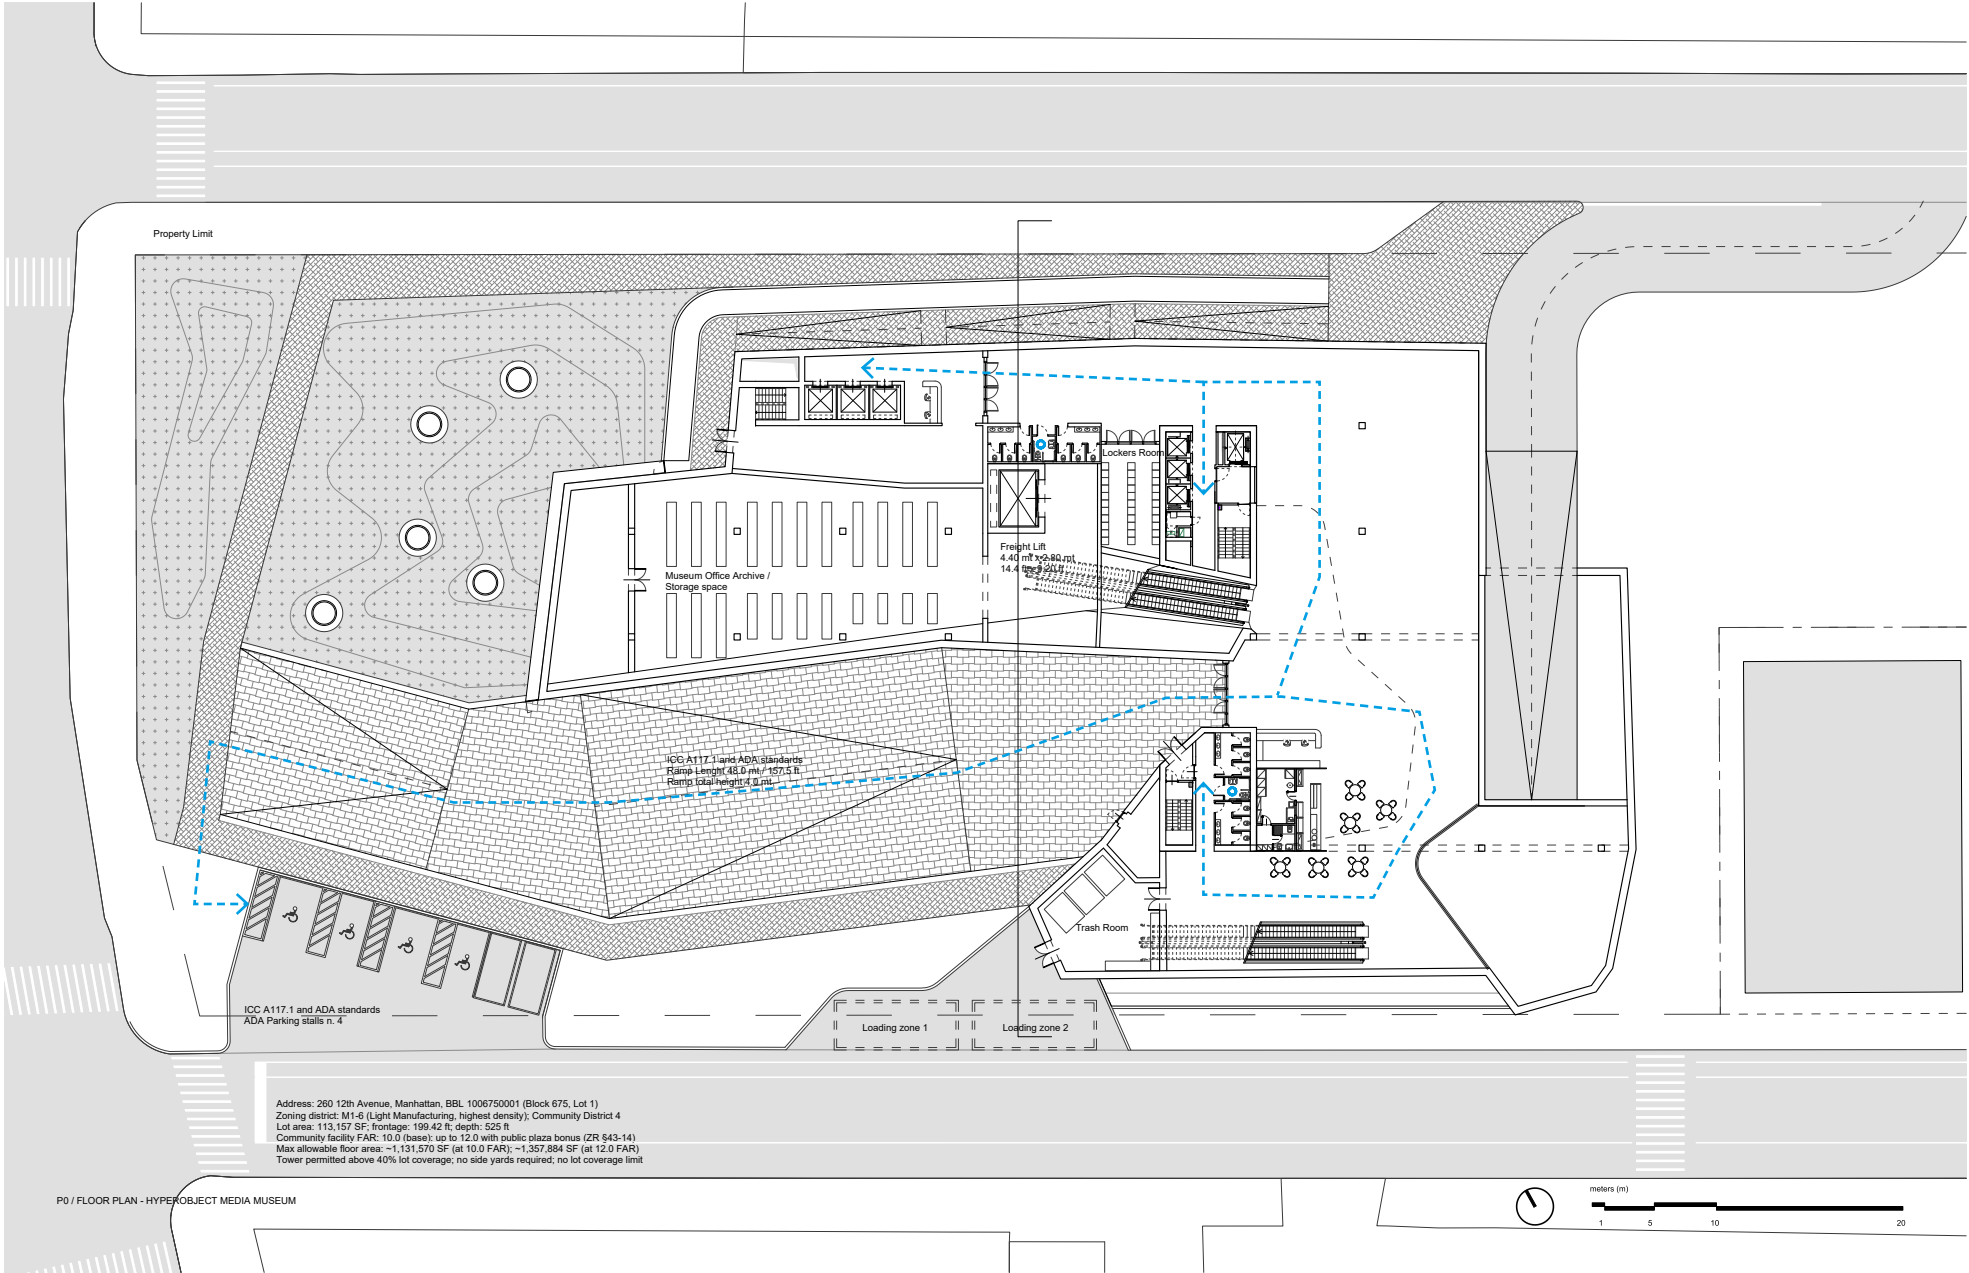

Egress Path Egress Turning Radius